

BẢN ĐỒ VỊ TRÍ, TỌA ĐỘ VÀ DIỆN TÍCH XIN THU HỒI ĐÁ ỚP LÁT VÀ ĐÁ LÀM VLXD THÔNG THƯỜNG
TẠI KHU VỰC THI CÔNG CÔNG TRÌNH NHÀ MÁY XỬ LÝ CTCN VÀ NH THUỘC XÃ TÀNG LOỎNG, TỈNH LÀO CAI.

(Kèm theo công văn số/CV-VS ngày / /2026 của Công ty CP dịch vụ xử lý Môi trường xanh Việt Sơn)

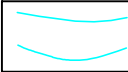
BẢNG TỌA ĐỘ CÁC ĐIỂM GÓC
DIỆN TÍCH KHU VỰC THU HỒI

Điểm góc	Hệ VN2000, kinh tuyến trục 104°45' múi chiều 3°	
	X(m)	Y(m)
1	2465259,1148	436993,1657
2	2465224,8025	437052,4652
3	2465180,4990	437155,0484
4	2465112,0891	437130,6785
5	2465095,9409	437089,3396
6	2465046,6645	437054,2762
7	2465021,8765	436998,8312
8	2465023,7012	436939,2555
9	2465067,6572	436877,5969
10	2465097,6020	436870,2844
11	2465162,6020	436887,1360
12	2465233,4657	436929,8148
Diện tích: 4,434 (ha)		

CHỈ DẪN

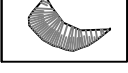
- 

Khu vực khai thác đá của dự án và đề xuất xin thu hồi đá khối làm đá ốp lát.
- 

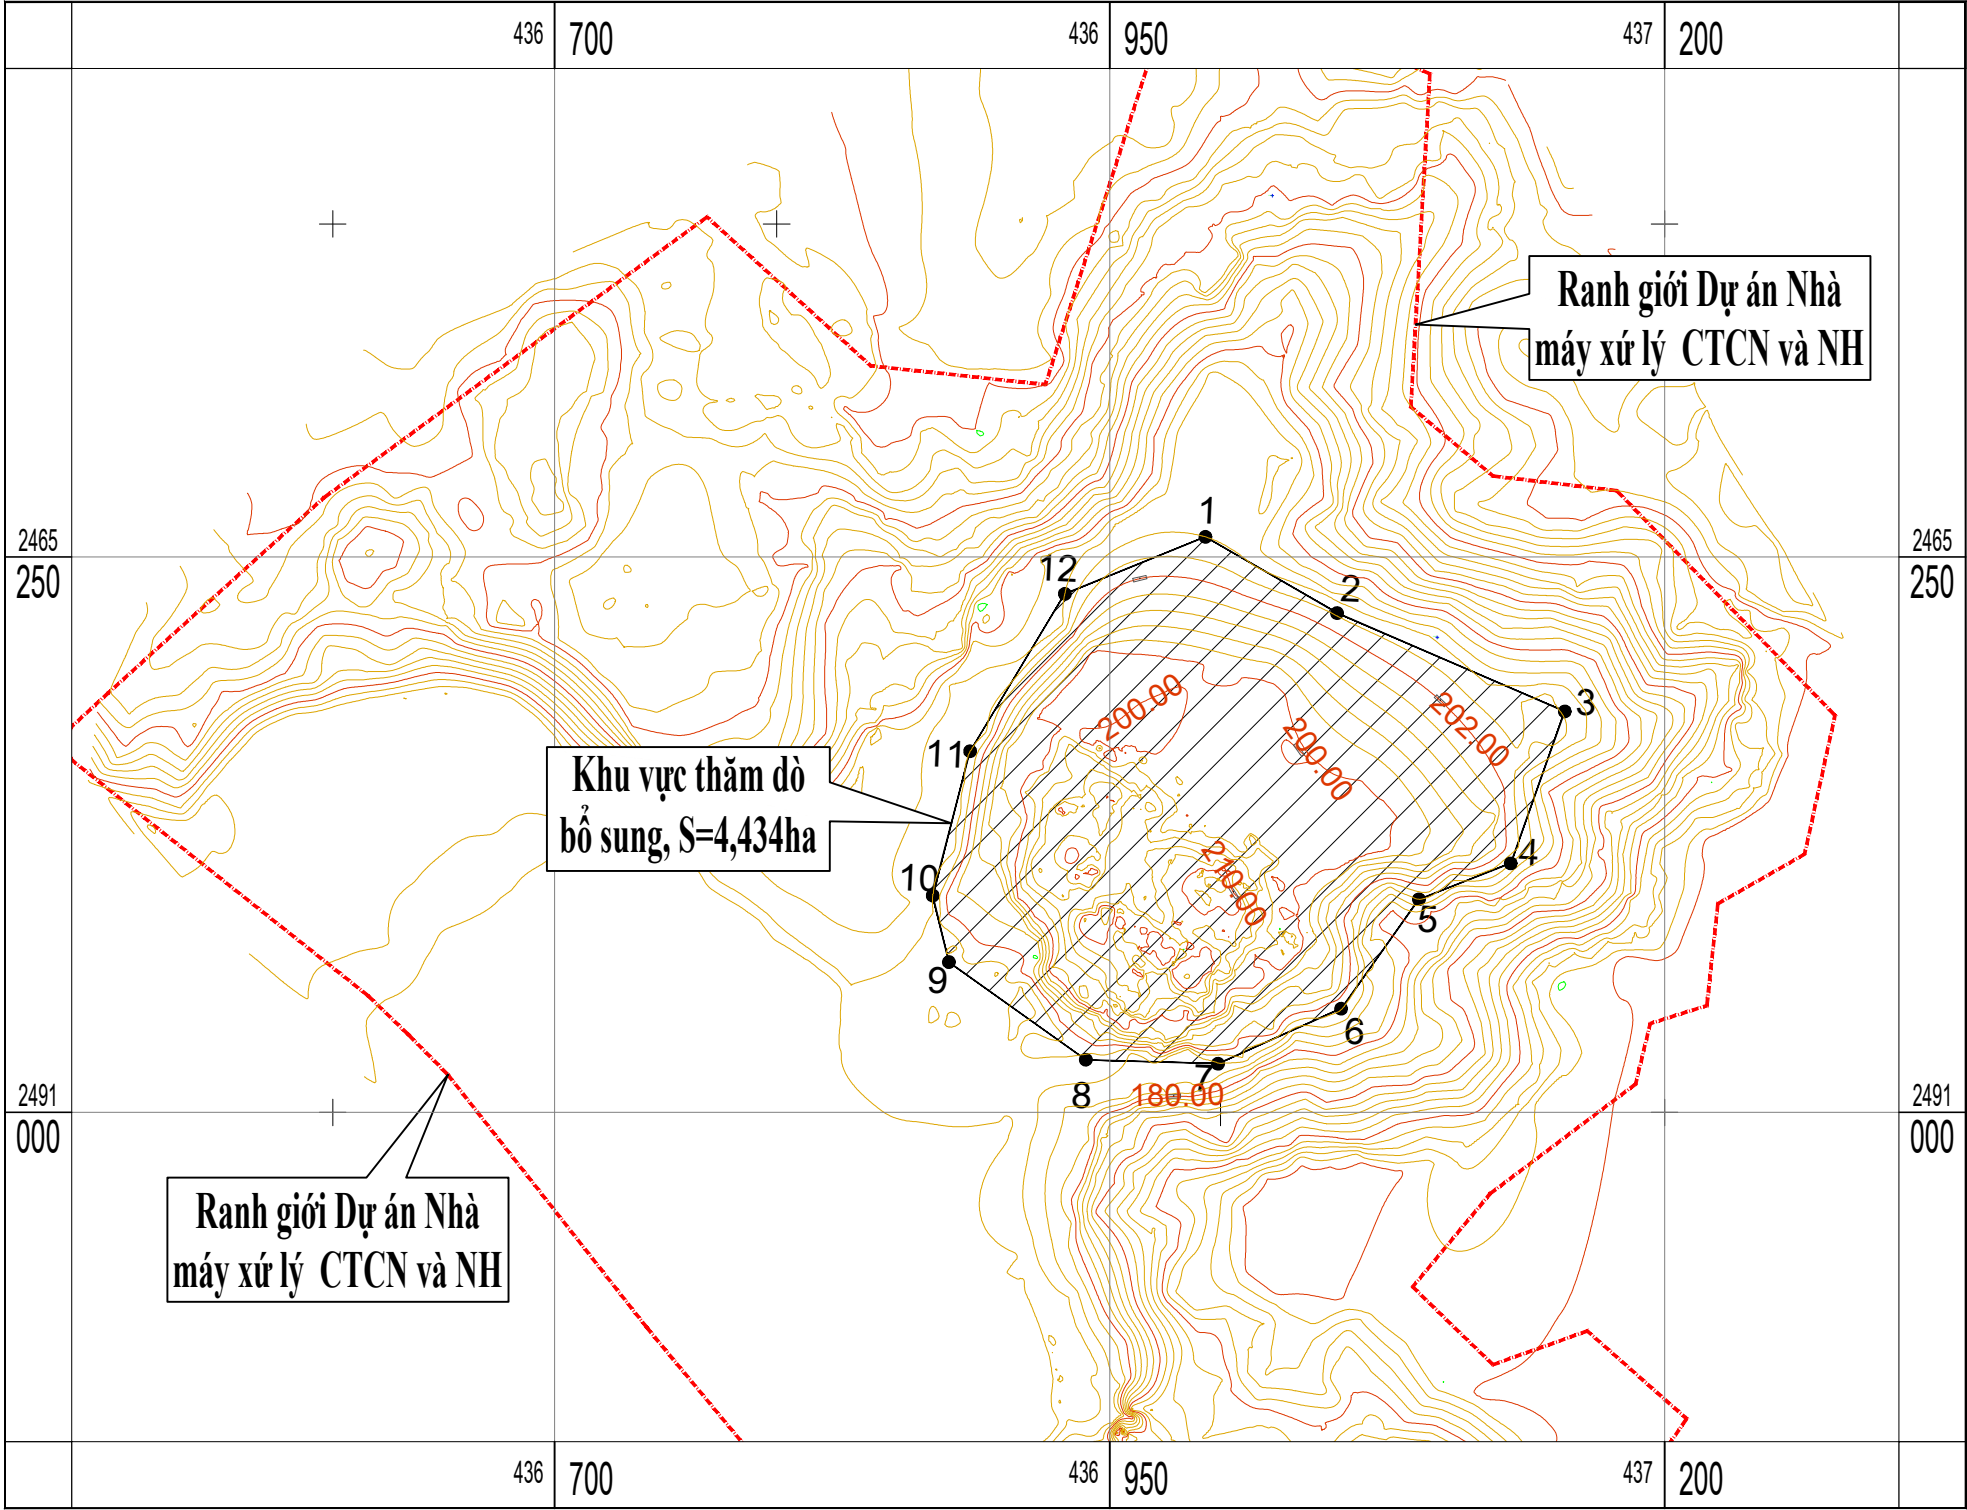
Ranh giới Khu vực dự án ĐT nhà máy xử lý CTCN và NH.
- 

Sông suối và hướng chảy.
- 

Đường giao thông.
- 

Đường đồng mức và độ cao.
- 

Taluy moong đã khai thác.



TỶ LỆ 1:5.000

**CÔNG TY CỔ PHẦN DỊCH VỤ
XỬ LÝ MÔI TRƯỜNG XANH VIỆT SƠN.**