


XÃ AN BÌNH

MẢNH TRÍCH ĐO ĐẠ CHÍNH THU HỒI ĐẤT SỐ 51 (1) -2020

HỆ TỌA ĐỘ VN - 2000, KHU VỰC: THÔN KHE RỒNG

TÊN CÔNG TRÌNH: DỰ ÁN XÂY DỰNG CƠ SỞ HẠ TẦNG GIAO THÔNG LIÊN VÙNG HỖ TRỢ
PHÁT TRIỂN KINH TẾ - XÃ HỘI CÁC HUYỆN NGHÈO TỈNH YÊN BÁI,
VAY VỐN QUỸ PHÁT TRIỂN ẨM-RẠP XÊ-ÚT (ĐOẠN TUYẾN KHÁNH HÒA - VĂN YÊN)

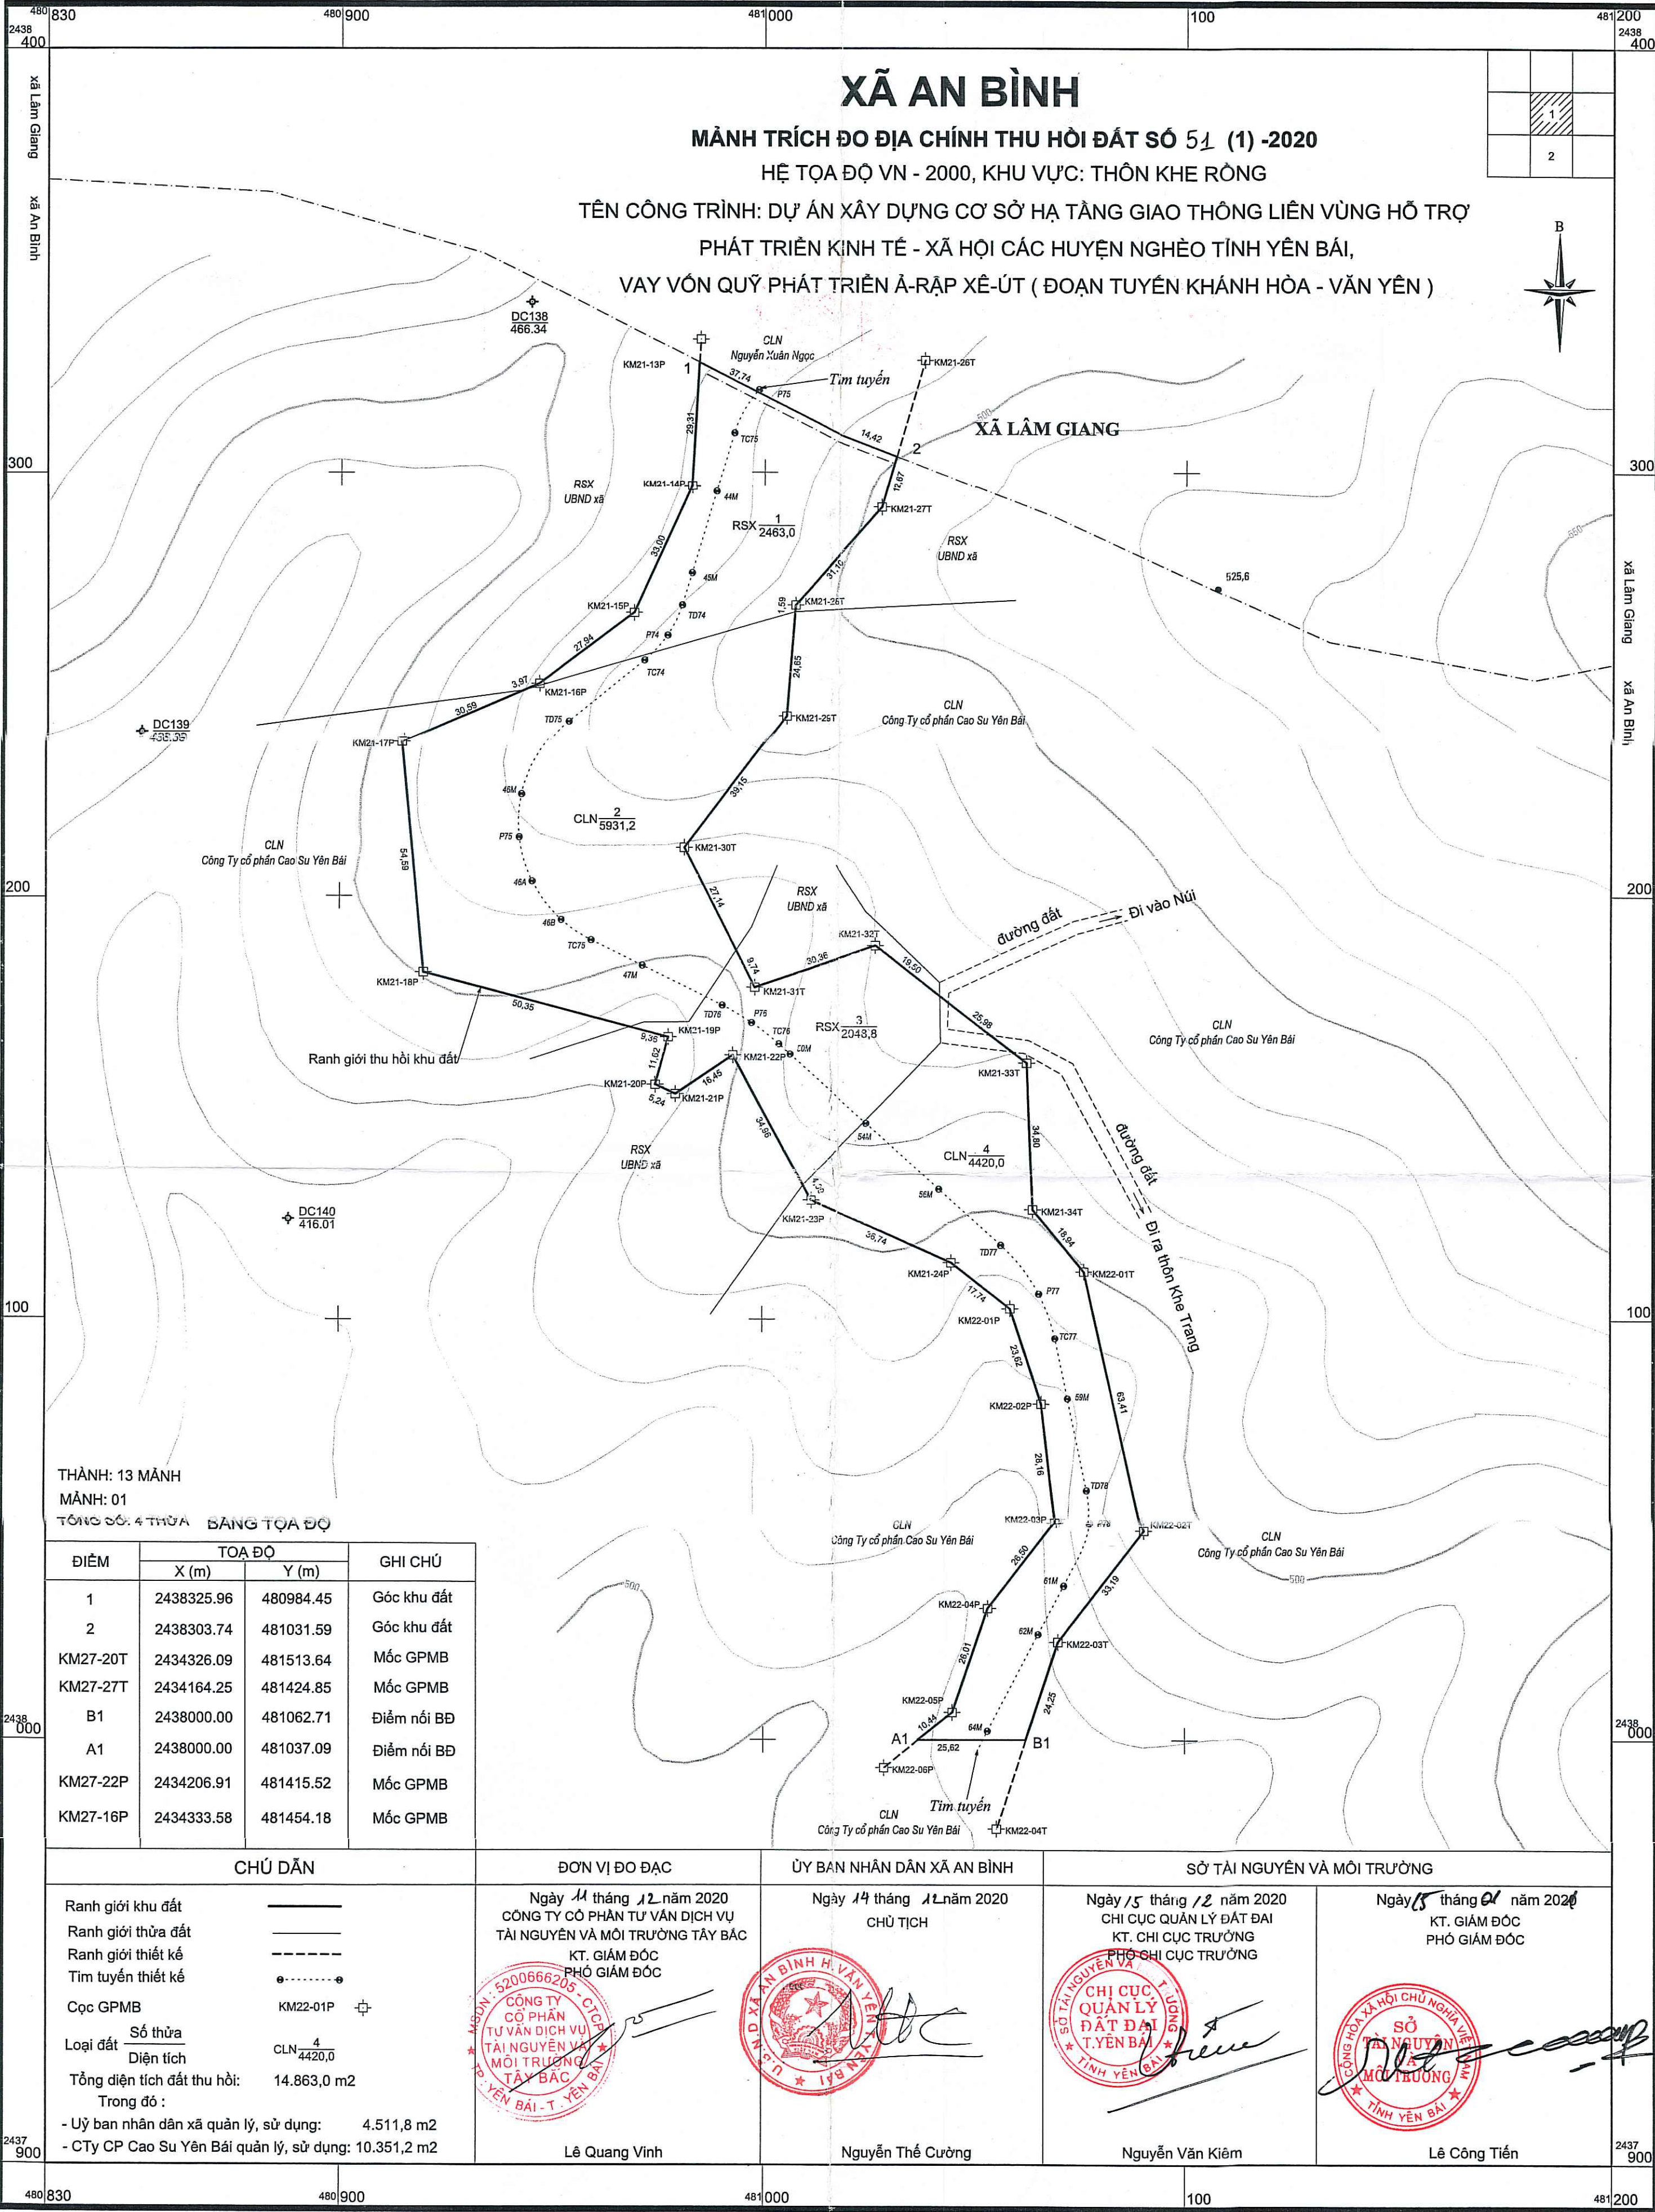

THÀNH: 13 MẢNH
MẢNH: 01
TỔNG SỐ: 4 THỪA BẢNG TỌA ĐỘ

ĐIỂM	TỌA ĐỘ		GHI CHÚ
	X (m)	Y (m)	
1	2438325.96	480984.45	Góc khu đất
2	2438303.74	481031.59	Góc khu đất
KM27-20T	2434326.09	481513.64	Mốc GPMB
KM27-27T	2434164.25	481424.85	Mốc GPMB
B1	2438000.00	481062.71	Điểm nối BĐ
A1	2438000.00	481037.09	Điểm nối BĐ
KM27-22P	2434206.91	481415.52	Mốc GPMB
KM27-16P	2434333.58	481454.18	Mốc GPMB

CHÚ DẪN	ĐƠN VỊ ĐO ĐẠC	ỦY BAN NHÂN DÂN XÃ AN BÌNH	SỞ TÀI NGUYÊN VÀ MÔI TRƯỜNG	
Ranh giới khu đất Ranh giới thửa đất Ranh giới thiết kế Tìm tuyến thiết kế Cọc GPMB Loại đất Diện tích Tổng diện tích đất thu hồi: Trong đó: - Ủy ban nhân dân xã quản lý, sử dụng: - CTy CP Cao Su Yên Bái quản lý, sử dụng:	Ngày 11 tháng 12 năm 2020 CÔNG TY CỔ PHẦN TƯ VẤN DỊCH VỤ TÀI NGUYÊN VÀ MÔI TRƯỜNG TÂY BẮC KT. GIÁM ĐỐC PHÓ GIÁM ĐỐC Lê Quang Vinh	Ngày 14 tháng 11 năm 2020 CHỦ TỊCH Nguyễn Thế Cường	Ngày 15 tháng 12 năm 2020 CHI CỤC QUẢN LÝ ĐẤT ĐAI KT. CHI CỤC TRƯỞNG PHÓ CHI CỤC TRƯỞNG Nguyễn Văn Kiêm	Ngày 18 tháng 01 năm 2021 KT. GIÁM ĐỐC PHÓ GIÁM ĐỐC Lê Công Tiến

TỶ LỆ 1:1000

